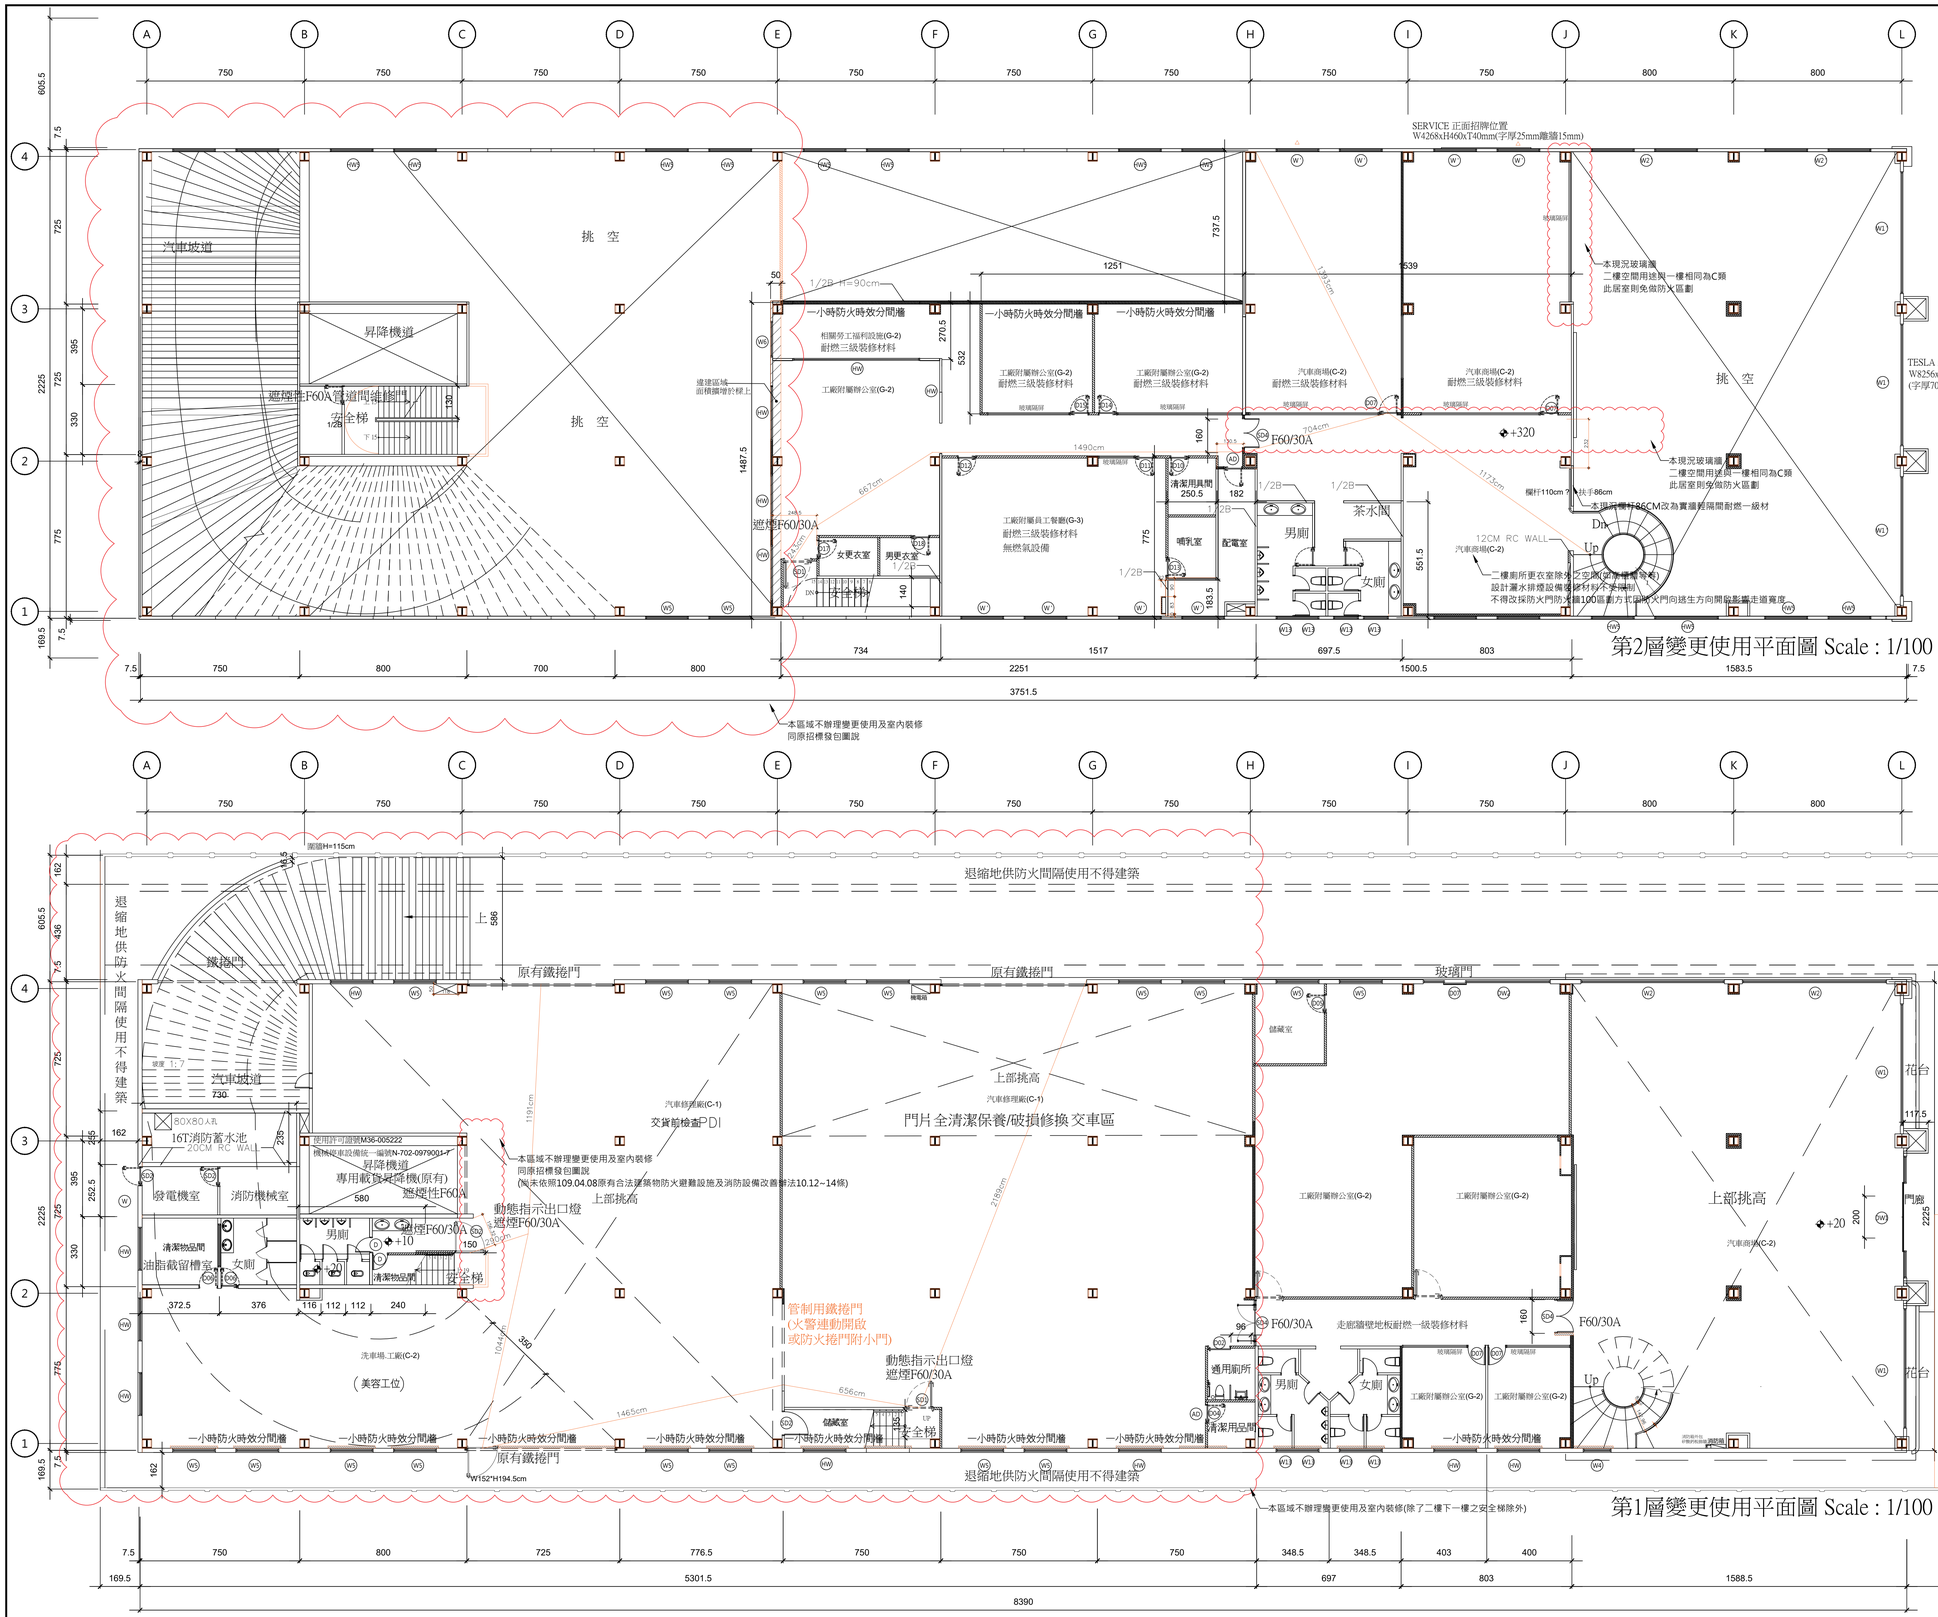

貳層面積(原核准)

廠房:37.515*14.875+15.39*7.375=671.54

樓梯間:3.30*8.0+21.6=48.09

合計:719.63

變更後

工廠附屬員工餐廳(G-3)

7.75*(15.17-1.82)-(2.505*1.835)=98.87㎡

相關勞工福利設施(G-2)

7.5*2.705=20.29㎡

汽車商場(C-2)

(7.50+7.50)*22.25-(7.50-6.975)*7.75+1.82*7.75+1.835*2.505=348.38㎡

工廠附屬辦公室(G-2)

719.63-98.87-20.29-348.38=252.09㎡

本區域不辦理變更使用及室內裝修
同原招標發包圖說

第2層變更使用平面圖 Scale : 1/100

壹層面積(原核准)

門廳:1.175*7.25=8.52

廠房:22.25*53.015-7.765*7.50=1121.35

辦公室:22.25*15.885+7.765*7.5+4.815*6.97=445.24

員工休息室:15.0*17.435+8.03*4.815=300.19

合計:1875.30

變更後

門廳 8.52㎡

洗車場.工廠(C-2)汽車修理廠(C-1) 1121.35㎡

汽車商場(C-2) 445.24㎡

工廠附屬辦公室(G-2)300.19㎡

第1層變更使用平面圖 Scale : 1/100

Client / 業主

TESLA

台灣特斯拉汽車有限公司
台北市內湖區瑞湖路二段1號
02 6610 3800

修 正
REVISIONS

日期		修 改 內 容
05	12	申請檔案圖說複印
05	23	查閱圖說及其影印圖本領取
05	26	業主校核
		內政部網路送件
		掛號
		初審會勘
		複審
		抽查
		核准

施工注意事項
Renovation considerations

應按照內政部建築解釋令規範新工法新設備新材料
審核認可通知書附圖及附錄規定施作之.
報告核准資料須檢附經濟部標準檢驗局證明,
並依建材商開立進貨數量出廠證明書.
上述證明應為輸入檢驗合格證書(進口品),或
商品驗證登錄書(國產品)如有新規定從其規定.
施工前承攬人應配合施工中消防安全防護計畫書
,依規定送交當地管轄消防隊核備後方可施工.
施工期間, 承攬人應按圖施工; 並應依法妥設安
全防護措施, 以維護現場及人員之安全.
應檢附之防火時效,耐燃,建材,防蝕,...證明,
防火門請明非製程提供時至少如下圖作需檢附
(在上角報告編號應作印).
標準檢驗則商品驗證登錄書•建築用防火門形式試驗
測試報告書•報告書內容目錄•申判案件基本資料•
試驗結果表•商品近照圖•測試作業程序記錄檢圖•
驗證登錄檢驗標誌位置示意圖•同型式判定報告書•
同型式判定結果•同型式尺寸檢視圖表•
可替換○○形式圖表•○○同型式引用對照表•
○○替換對照表•報告書中五金之詳圖前視圖標模
○○平面圖•製造商出廠證明.....
其他證明如下
內政部建築新材料認可通知書及其
自主查核表與標準施工圖
標檢照之輸入檢驗合格證,輸入品商驗證明,
商品驗證登錄證書,製造商出廠證明,
經選材標準証書.....
施工前台電屬內線路檢驗紀錄單,台電派員檢查結果通
過選材使用率≥60%

設計施工地點

台南市南區新樂路22號1~4樓
南區鹽埕段26131建號
南區鹽埕段3085-0009地號

(090)南工造字第00195號
(91)南工使字第469號

設計施工廠商

Architects
郭子文建築師事務所
Interior Designer
齊雲室內裝修工程有限公司
Fire-Fighting Facilities Designer
開安消防公司 王查勝
Structure Designer

M&E Engineering Designer

Air-Conditioning Equipment Designer
玉鼎空調技師事務所 鄭翰陽
Landscape Gardening Designer

Performance-based Design of Fire Safety and Evac

工程名稱 PROJECT
台灣特斯拉汽車有限公司
台南保養修理銷售交車中心

審核 SPONSOR 郭子文
首次送證 UNDERTAKE 12'May.2022
網路序號 ORDINAL NUMBER
掛號號碼 REGISTRATION
出圖 ISSUED FOR 國建
掛號日期 DATE

建築師簽印欄

圖名 DRAWING TITLE

變更使用圖說審查執照圖
☑ 一樓與二樓平面圖
☑ 法規檢討
☑ 區劃位置圖

圖號 DRAWING NUMBER
A2
2/3
scale:1/200以上